TOPOGRAPHIC MAP SHOWING EXISTING CONDITIONS UPON

LOT 10, PART B
of "THE LALAMILO FARM LOTS"
Being portion of R. P. 5671, L. C. Aw. 852l-B, Part 1 to G. D. Hueu conveyed to the Territory of Hawaii (now State of Hawaii) by Richard Smart by Deed dated June 12, 1956 and recorded in Liber 3126, Pages 36-55 (Land Office Deed 13596), at Lalamilo and Waikoloa, Waimea, South Kohala, State of Hawaii
TMK (3) 6-6-005:003-0000

NOTE: BASIS OF AZIMUTH DERIVED USING HEMISPHERE GPS RTK SYSTEM


NOTE: ALL AZIMUTHS & DISTANCES ARE SHOWN & MAPPED HEREON IN A CLOCKWISE DIRECTION

LEGEND	
IV=	IRRIGATION VALVE
	CONCRETE

TRUE NORTH

0 60

SCALE ONE INCH EQUALS 60.00 FEET

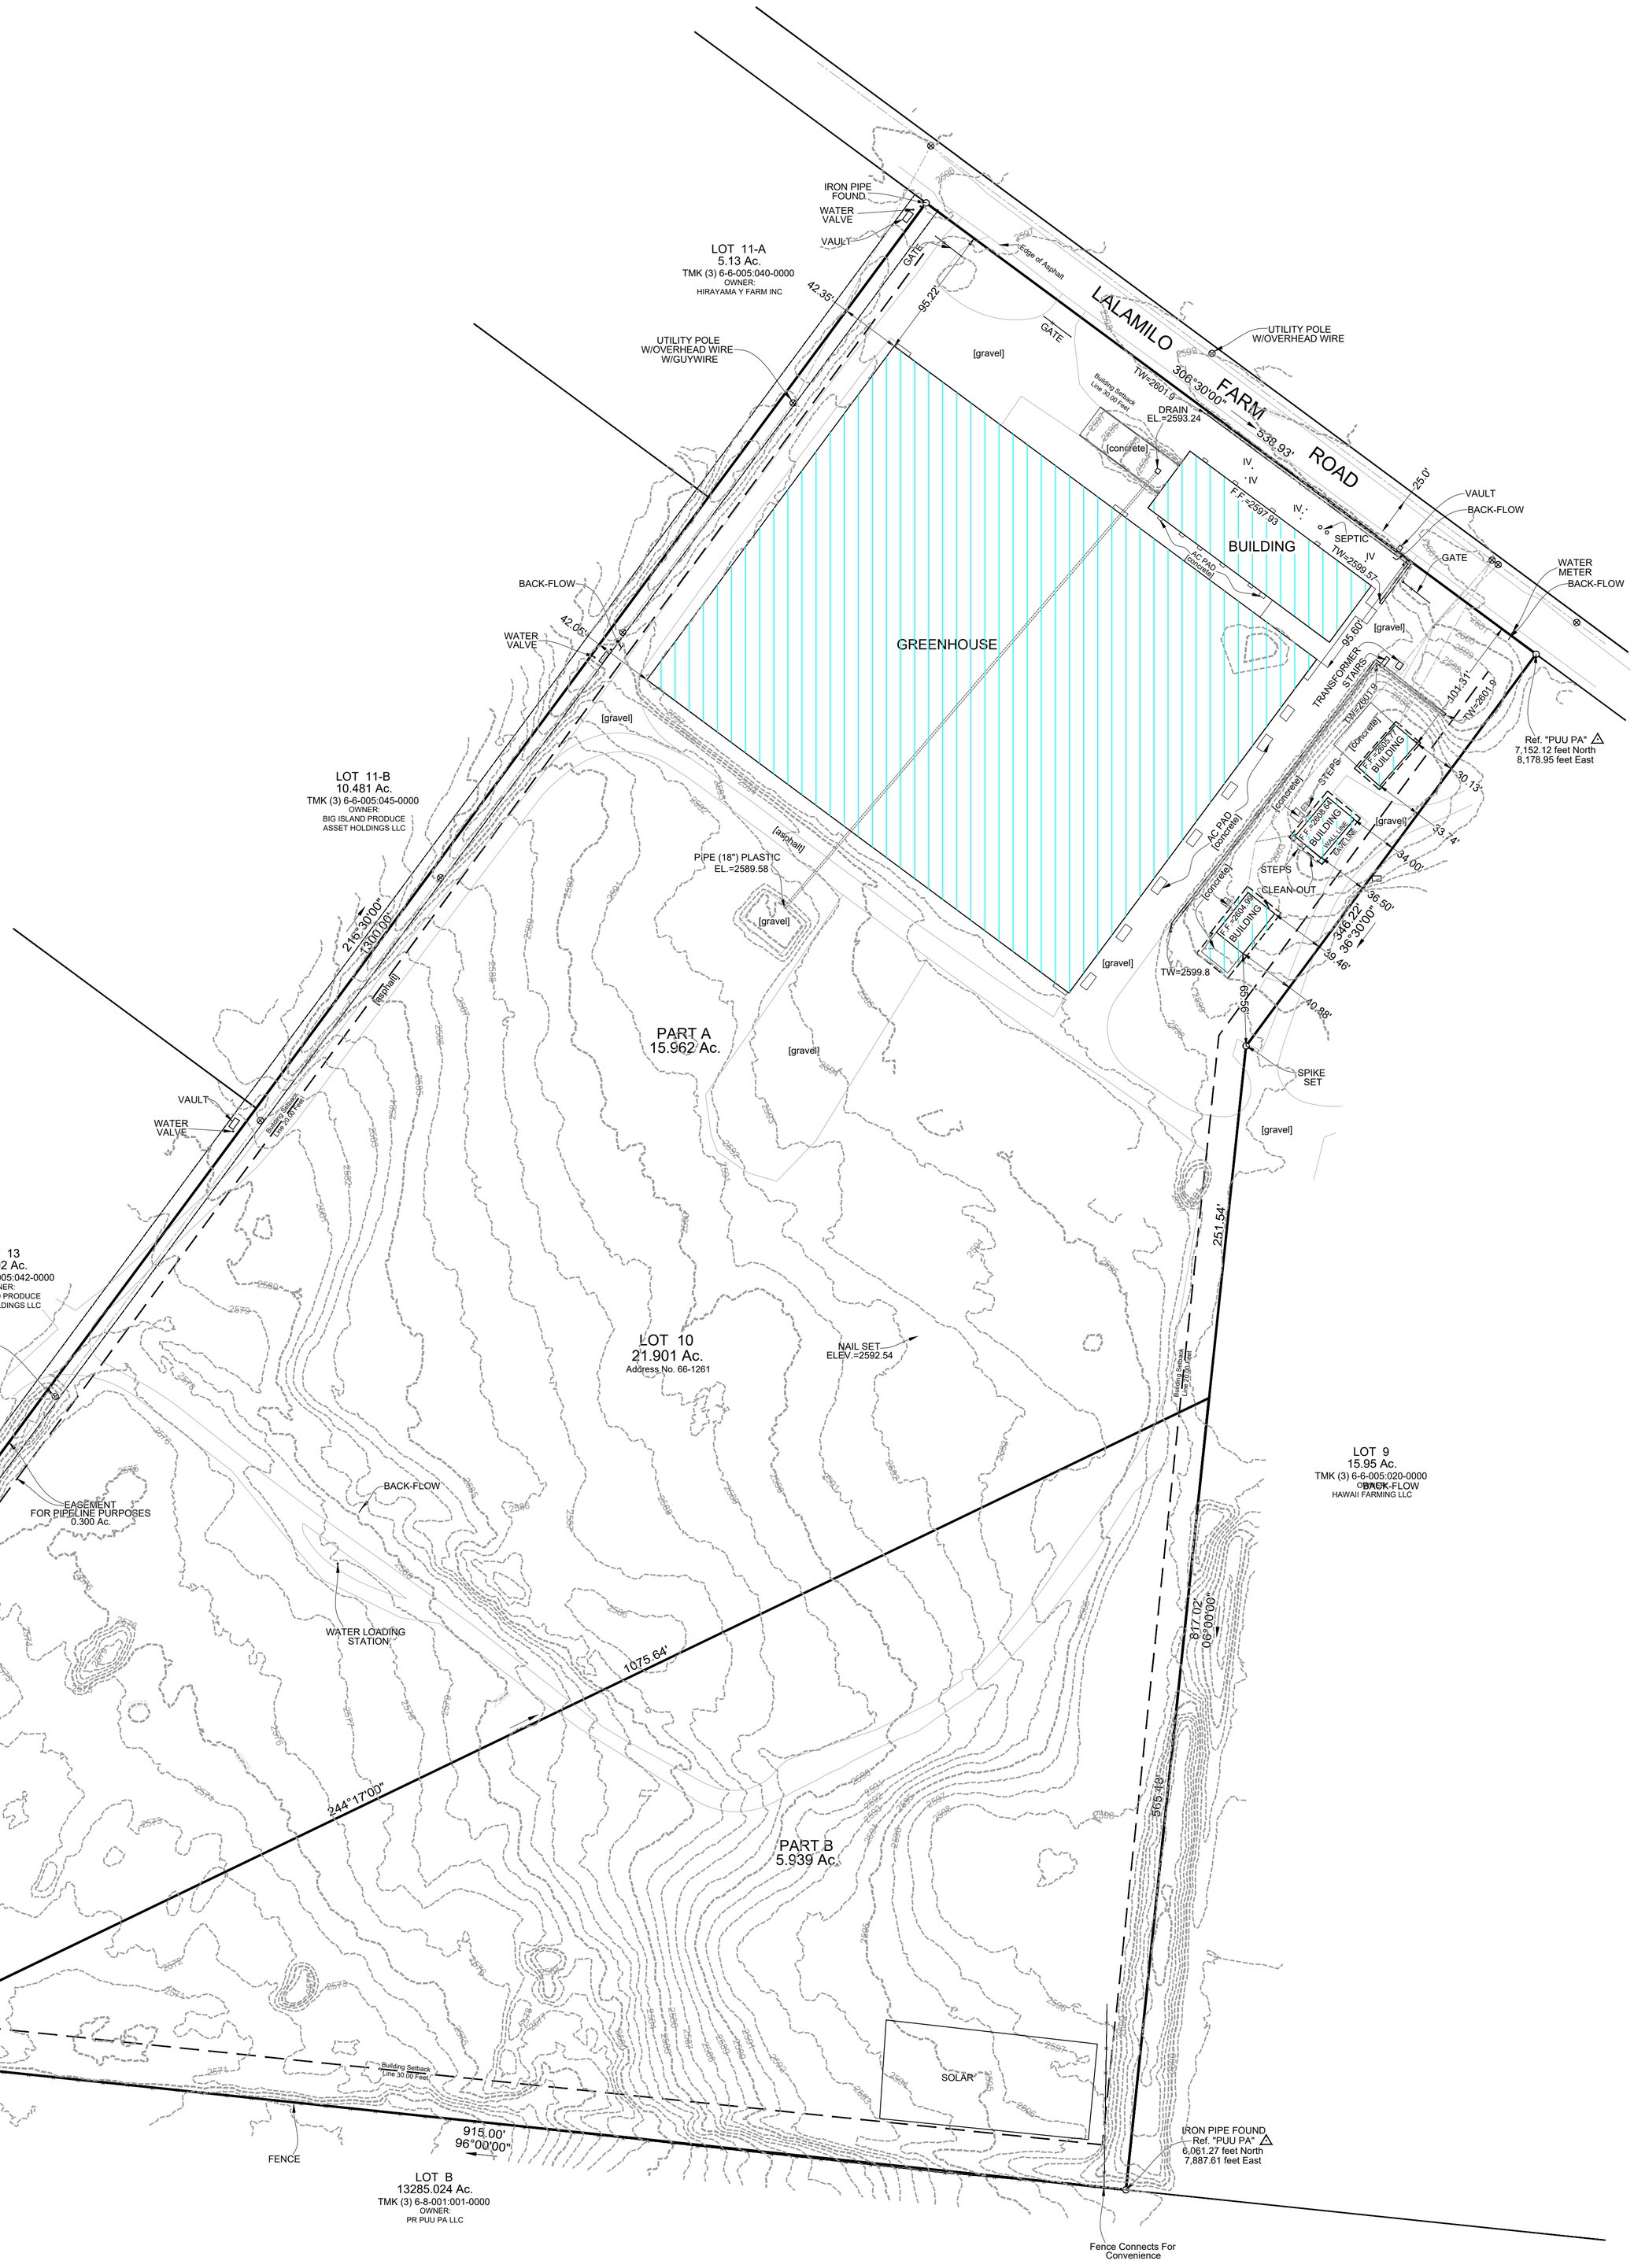

FLOOD NOTE

According to the F.I.R.M. # 155166 0193 F, dated 09-29-2017 this property does lie in "Zone X".

NOTES:

1) **The distances shown between the property lines & the features, shown hereon, are based on selected found boundary monuments & acceptable tolerances for properties of this type.**
2) **The features shown and mapped hereon were located by an actual survey performed on the ground on December 3rd, 2025.**
3) **Elevations shown and mapped hereon are based on an Opus Static Solution.**
4) **SCALE: One inch equals feet 1"= 60'**
5) **Contour Interval: Major 5' & Minor 1'**

I, Thomas G. Pattison, do hereby certify to the best of my professional knowledge, information, and belief that this map and the survey upon which it is based correctly shows the boundary lines and topographic features as shown on the ground.

-COPY-

THOMAS G. PATTISON
January 5th, 2026
Hawaii License No. 10743

Setback Lines are shown from current data, but should be verified by builder. The description on this plat was provided to us by the client, and does not guarantee ownership, and should be compared to your Deed, Abstract or Certificate of Title. All building restrictions, building lines and easements may or may not be shown, check your Deed, Abstract, Title Report, and local ordinances, no responsibility is assumed by Surveyor. Compare all points before building by same and report any discrepancy at once. Dimensions are shown in feet and decimal parts thereof, no dimension is to be assumed by scaling.

PATTISON LAND SURVEYING | P.O. Box 384569 • Waikoloa Hawaii • 96738 • Office 808.327.9439 •